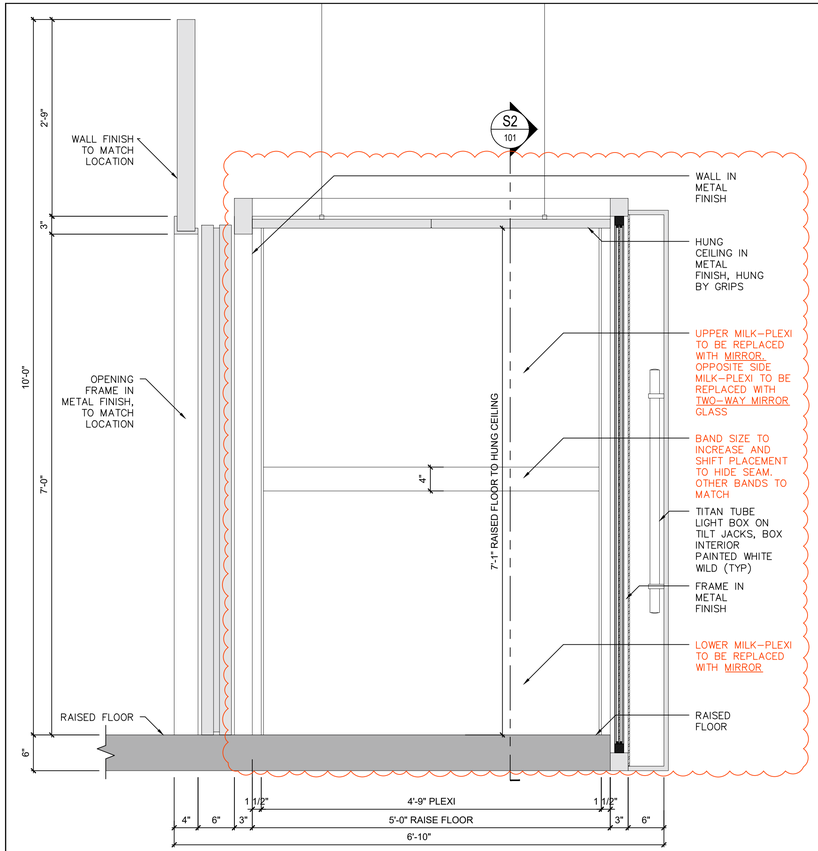

S1 101 SECTION - ELEVATOR CAB INTERIOR
SCALE 1"=1'

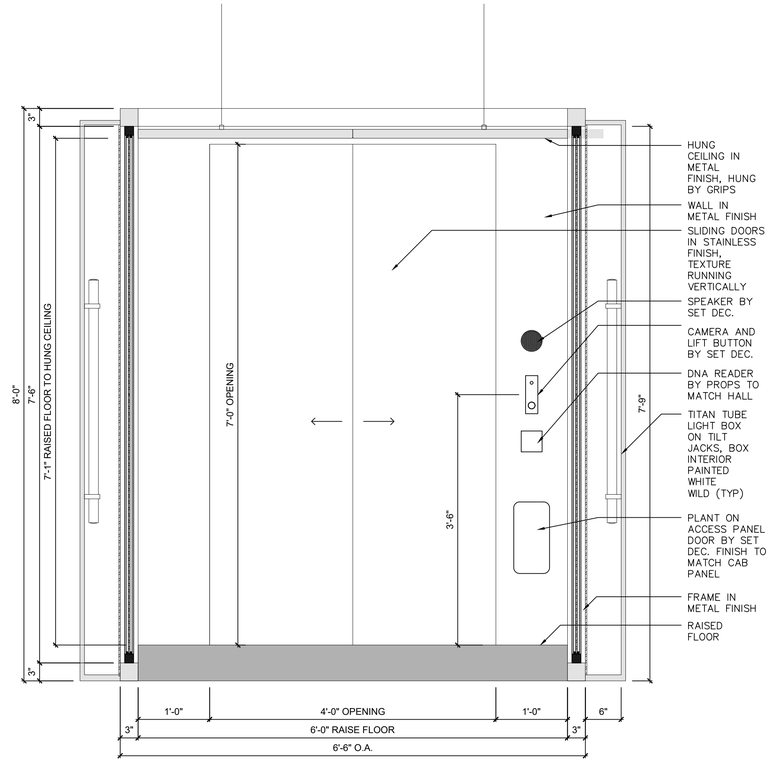

E1 101 ELEVATION - ELEVATOR CAB INTERIOR
SCALE 1"=1'

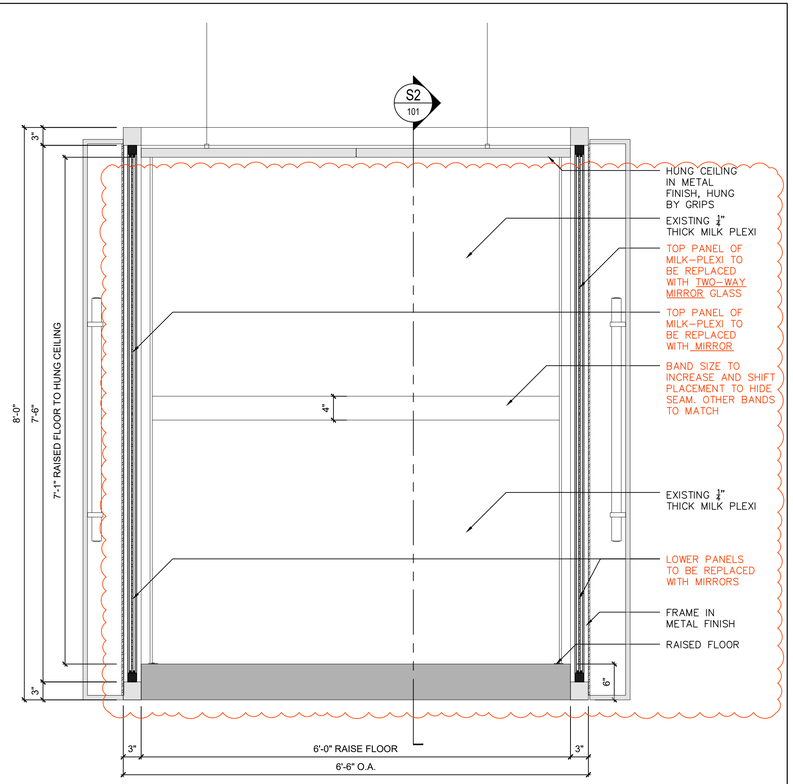

E2 101 ELEVATION - ELEVATOR CAB INTERIOR
SCALE 1"=1'

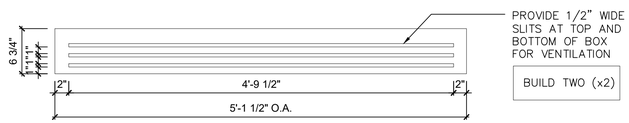

P1 101 PLAN - LIGHT BOX (TYPE 1)
SCALE 1"=1'

E3 101

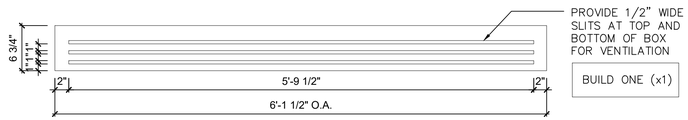

P2 101 PLAN - LIGHT BOX (TYPE 2)
SCALE 1"=1'

E4 101

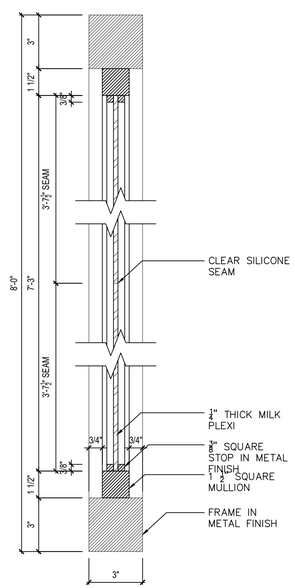

S2 101 SECTION - ELEVATOR CAB WALL
SCALE 3"=1'

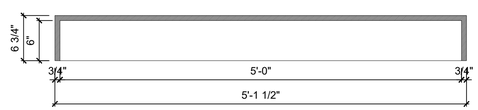

S3 101 SECTION - LIGHT BOX (TYPE 1)
SCALE 1"=1'

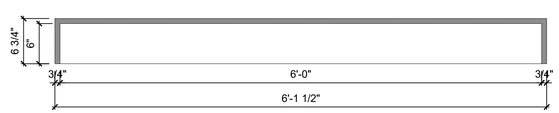

S4 101 SECTION - LIGHT BOX (TYPE 2)
SCALE: 1" = 1'

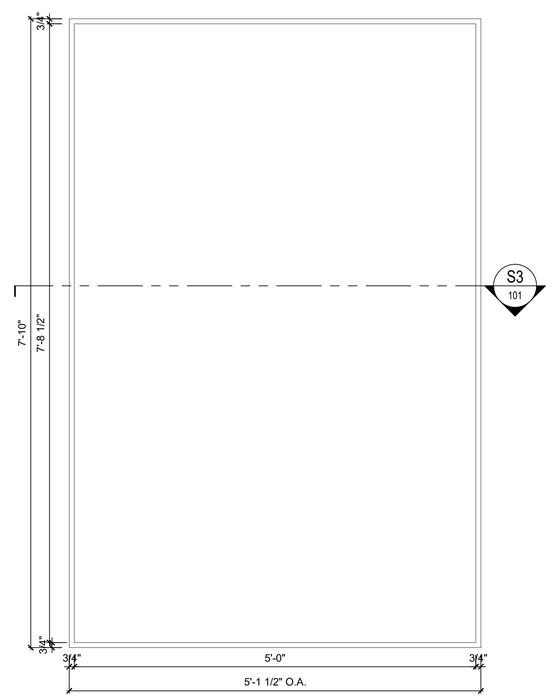

E3 101 ELEVATION - LIGHT BOX (TYPE 1)
SCALE 1"=1'

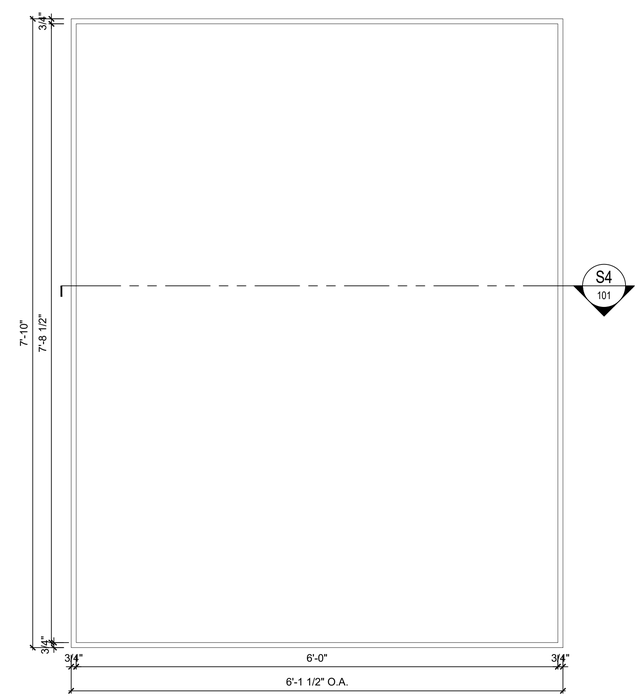

E4 101 ELEVATION - LIGHT BOX (TYPE 2)
SCALE 1"=1'

REVISED
DEC 05/22

ORPHAN BLACK: ECHOES	ORPHAN BLACK SPINOFF PRODUCTIONS LTD. 2480 STANFIELD RD. MISSISSAUGA, ON, L9Y1S2 T: 647.689.8010	Production Designer: AIDAN LEROUX	Set name.: INT. ADDITIVE FOUNDATION - ELEVATOR	Date: SEP 19, 2022	Scale: AS NOTED	Revised: DEC 05, 2022	Revision no.: 04
		Art Director: ALDER DUNLAP	Location address: STUDIO	Drawn by: A.L., E.S.	Sheet name: ELEVATIONS		

Set no.: S028 | Sheet no.: 101