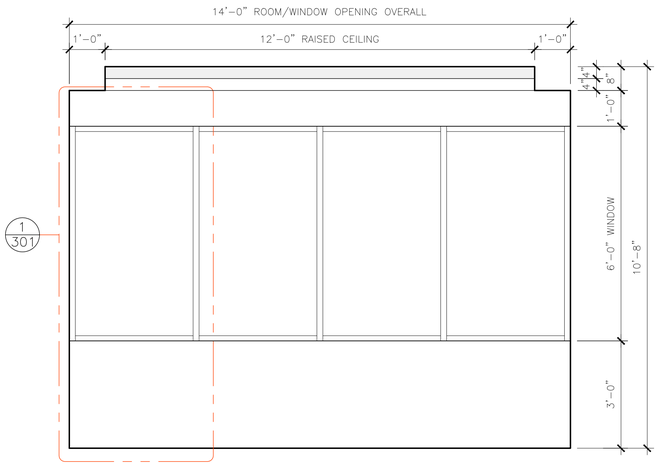

1 / 201 JULES' BEDROOM WINDOW ELEVATION
SCALE: 1/2" = 1'-0"

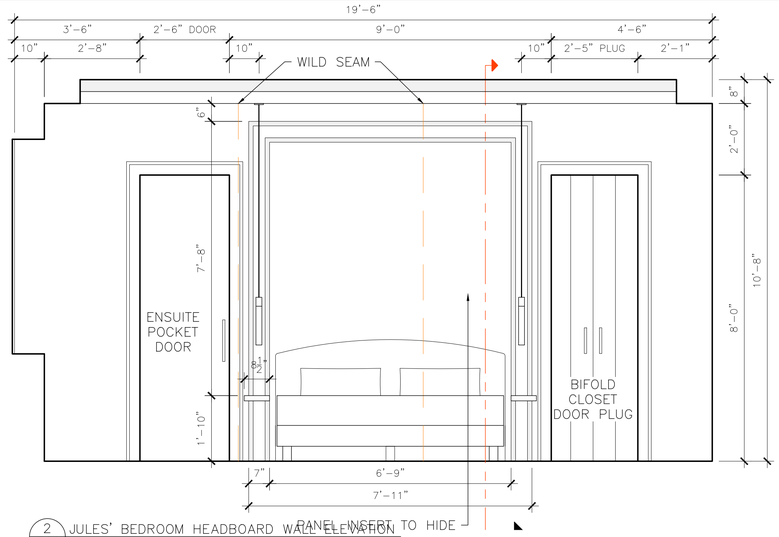

2 / 201 JULES' BEDROOM HEADBOARD WALL ELEVATION
SCALE: 1/2" = 1'-0"

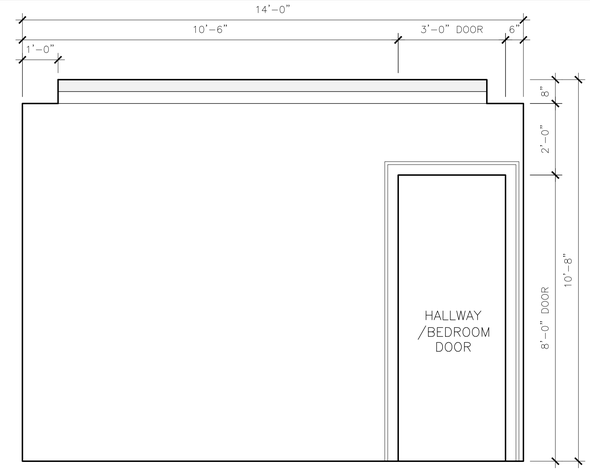

3 / 201 JULES' BEDROOM ENTRANCE ELEVATION
SCALE: 1/2" = 1'-0"

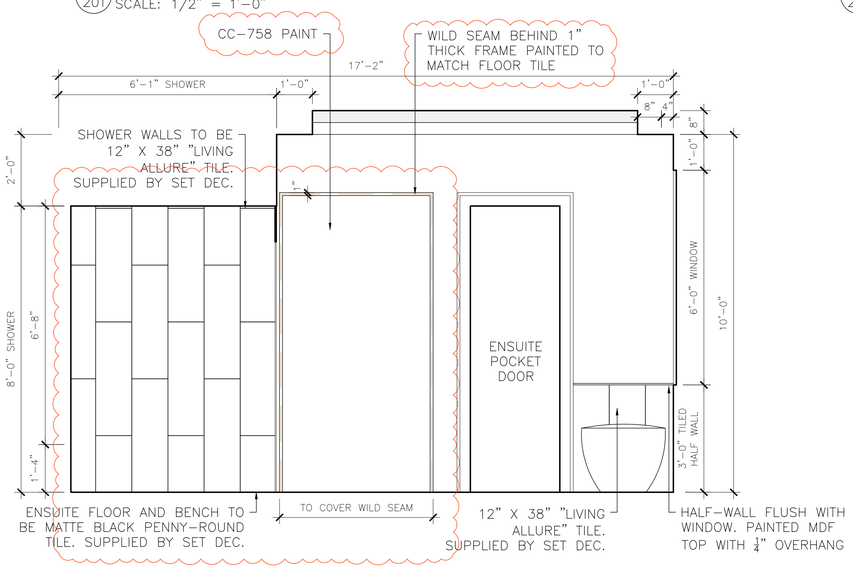

4 / 201 JULES' ENSUITE ENTRANCE/SHOWER ELEVATION
SCALE: 1/2" = 1'-0"

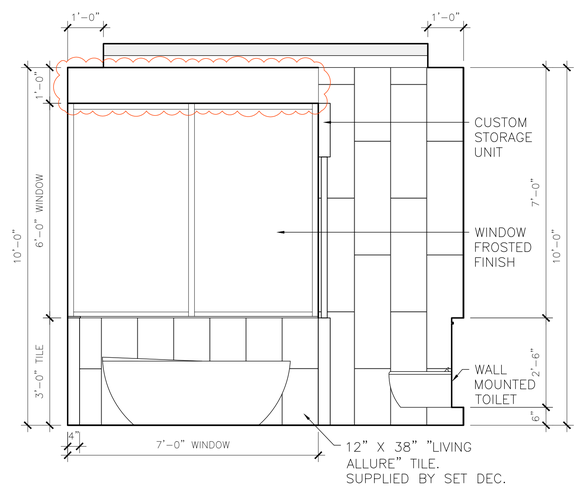

5 / 201 JULES' ENSUITE WINDOW ELEVATION
SCALE: 1/2" = 1'-0"

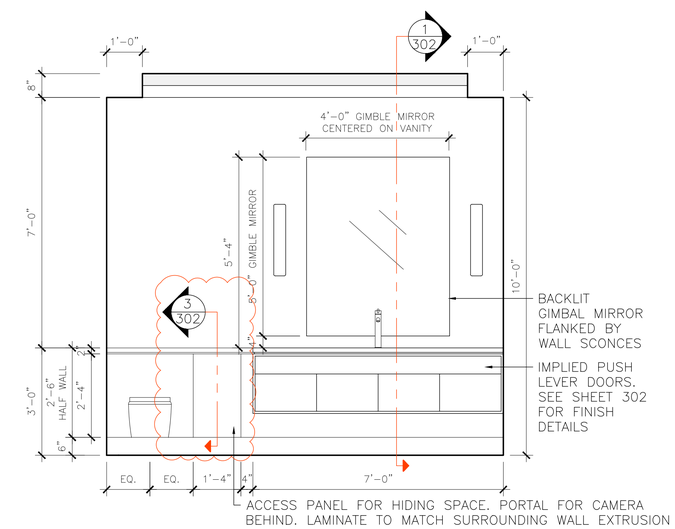

6 / 201 JULES' ENSUITE ELEVATION
SCALE: 1/2" = 1'-0"

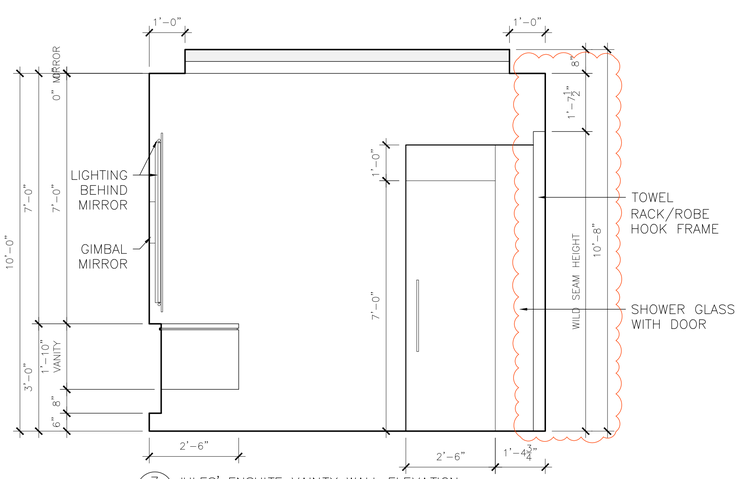

7 / 201 JULES' ENSUITE VAINTY WALL ELEVATION
SCALE: 1/2" = 1'-0"

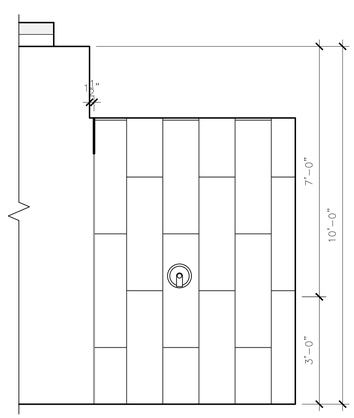

8 / 201 JULES' SHOWER/ALCOVE WALL ELEVATION
SCALE: 1/2" = 1'-0"

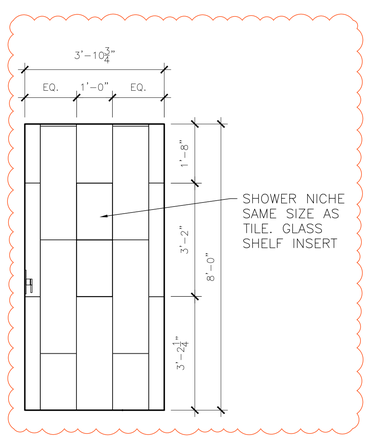

9 / 201 JULES' SHOWER ELEVATION
SCALE: 1/2" = 1'-0"

REVISED
SEP 29/22

ORPHAN BLACK: ECHOES	ORPHAN BLACK SPINOFF PRODUCTIONS LTD. 2480 STANFIELD RD. MISSISSAUGA, ON, L5Y1S2 T: 647.689.8010	Production Designer: ADAIN LEROUX	Set name.: INT_JULES' CONDO	Date: AUG 31, 2022	Scale: AS NOTED	Revised: SEP 29, 2022	Revision no.: 06	Set no.: S041
		Art Director: ALDER DUNLAP	Location address: STUDIO	Drawn by: E.S.	Sheet name: ELEVATIONS			Sheet no.: 201