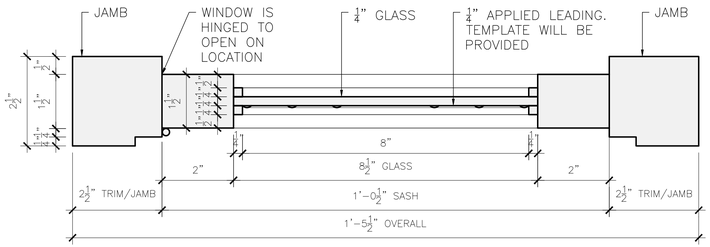

1/302 FOYER WINDOW SECTION
SCALE: 6" = 1'-0"

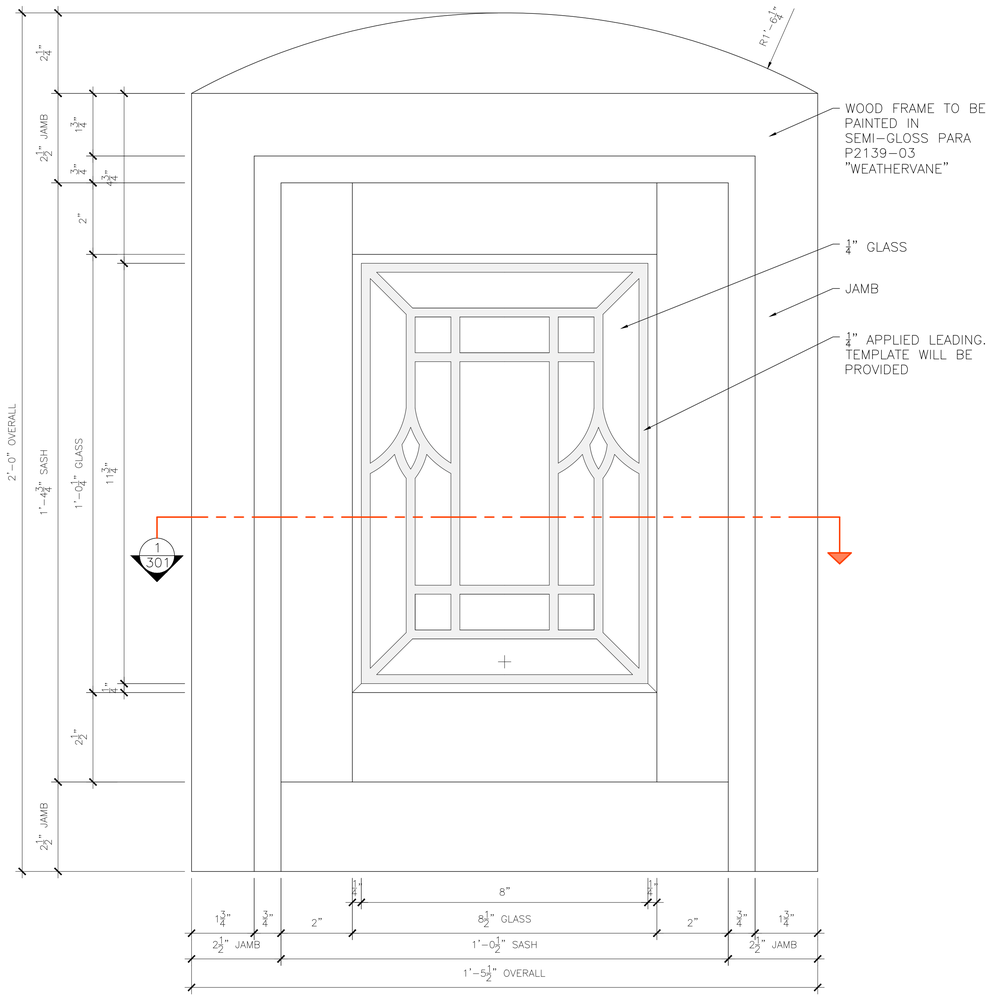

2/302 FOYER WINDOW SECTION
SCALE: 6" = 1'-0"

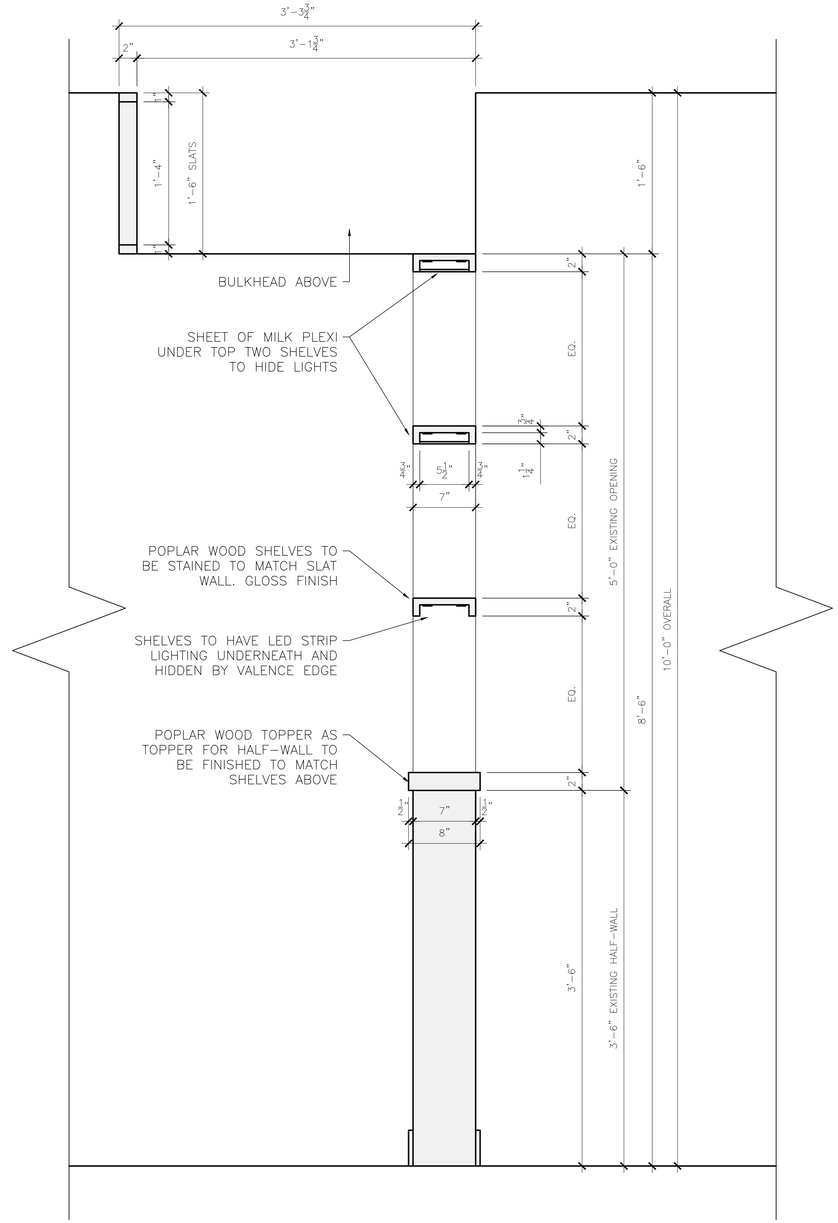

3/302 LIVING ROOM SHELVING SECTION
SCALE: 1-1/2" = 1'-0"

GENERAL NOTES
1. ALL TRIM TO BE PAINTED IN SEMI-GLOSS PARA P2139-03 "WEATHERVANE"

REVISED
AUG 25/22

ORPHAN BLACK: ECHOES	ORPHAN BLACK SPINOFF PRODUCTIONS LTD. 2480 STANFIELD RD. MISSISSAUGA, ON, L9Y1S2 T: 647.689.5010	Production Designer: AIDAN LEROUX	Set name.: INT. TINA'S HOUSE	Date: AUG 22, 2022	Scale: AS NOTED	Revised: AUG 25, 2022	Revision no.: 02	Set no.: S020	Sheet no.: 302
		Art Director: ALDER DUNLAP	Location address: STUDIO	Drawn by: E.S.	Sheet name: DETAILS				