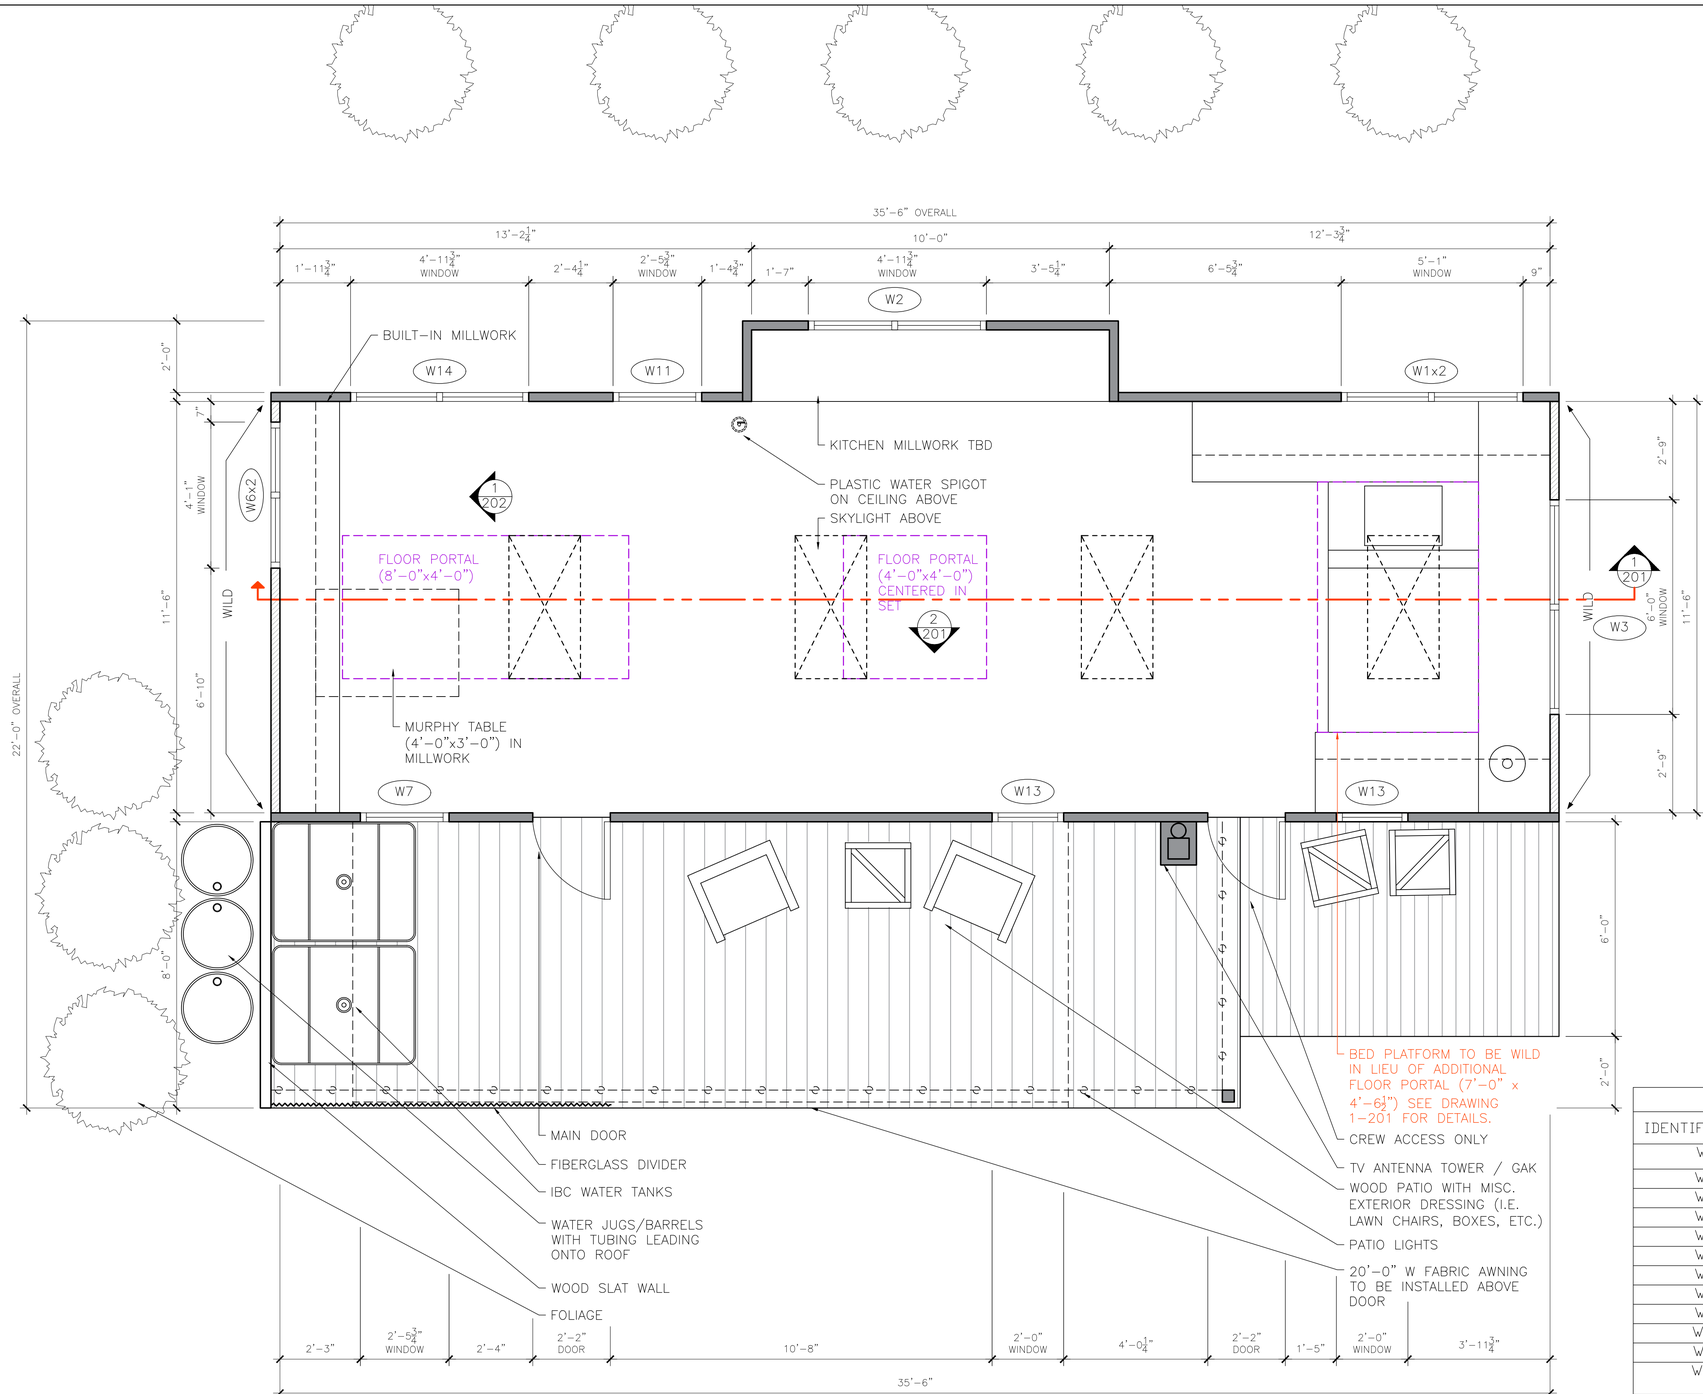

1 INT. TRAILER STUDIO SET PLAN
101 SCALE: 1/2" = 1'-0"

SCRIPT 101 NOTES:

- PLASTIC SPIGOT HANGING FROM CEILING [12]
- BUILT-IN PANEL ABOVE BED [12]
- SHELVES WITH BOOKS & TECHNICAL MANUALS [12]
- VINYL RECORD COLLECTION [12]
- RECORD PLAYER [18]
- OLD SPEAKER SYSTEM [18]
- SMALL BED [19]
- EXPOSED RUBBER TUBING (WATER SYSTEM) [33]

WINDOW SCHEDULE

IDENTIFICATION	WIDTH (INCHES)	HEIGHT (INCHES)	STATE	FINISH	NOTES
W1	29 3/4	22	USED	N/A	2 PANES HIGH
W2	148 1/4	22	USED	N/A	3 PANES HIGH
W3	71 3/4	22	USED	N/A	3 PANES HIGH
W4	23 3/4	29	USED	N/A	4 PANES HIGH
W5	35 3/4	22	USED	N/A	3 PANES HIGH
W6	23 3/4	15	USED	N/A	2 PANES HIGH
W7	29 3/4	29	USED	N/A	4 PANES HIGH
W8	29 3/4	15	USED	N/A	2 PANES HIGH
W9	59 3/4	18	USED	N/A	HALF & HALF
W10	47 3/4	18	USED	N/A	2 PANES HIGH
W11	29 3/4	15	USED	N/A	2 PANES HIGH
W12	29 3/4	44	USED	N/A	REGULAR WINDOW
W13	24	34 1/4	USED	N/A	5 PANES HIGH
W14	59 3/4	18	USED	N/A	HALF & HALF

GENERAL NOTES

1. CEILING TO BE CONSTRUCTED WITH 2"x4" STUDS TO BEAR WEIGHT OF DRESSING, ACTORS, CREW, ETC.

ISSUED
AUG 08/22

ORPHAN BLACK: ECHOES

ORPHAN BLACK SPINOFF PRODUCTIONS LTD.
2480 STANFIELD RD.
MISSISSAUGA, ON, L5Y1S2
T: 647.689.8010

Production Designer: AIDAN LEROUX	Set name: INT. LUCY'S TRAILER	Date: AUG 08 - 2022	Scale: AS NOTED	Revised:	Revision no.:	Set no.: S005	Sheet no.: 101
Art Director: ALDER DUNLAP	Location address: STUDIO	Drawn by: E.S.	Sheet name: FLOOR PLAN				