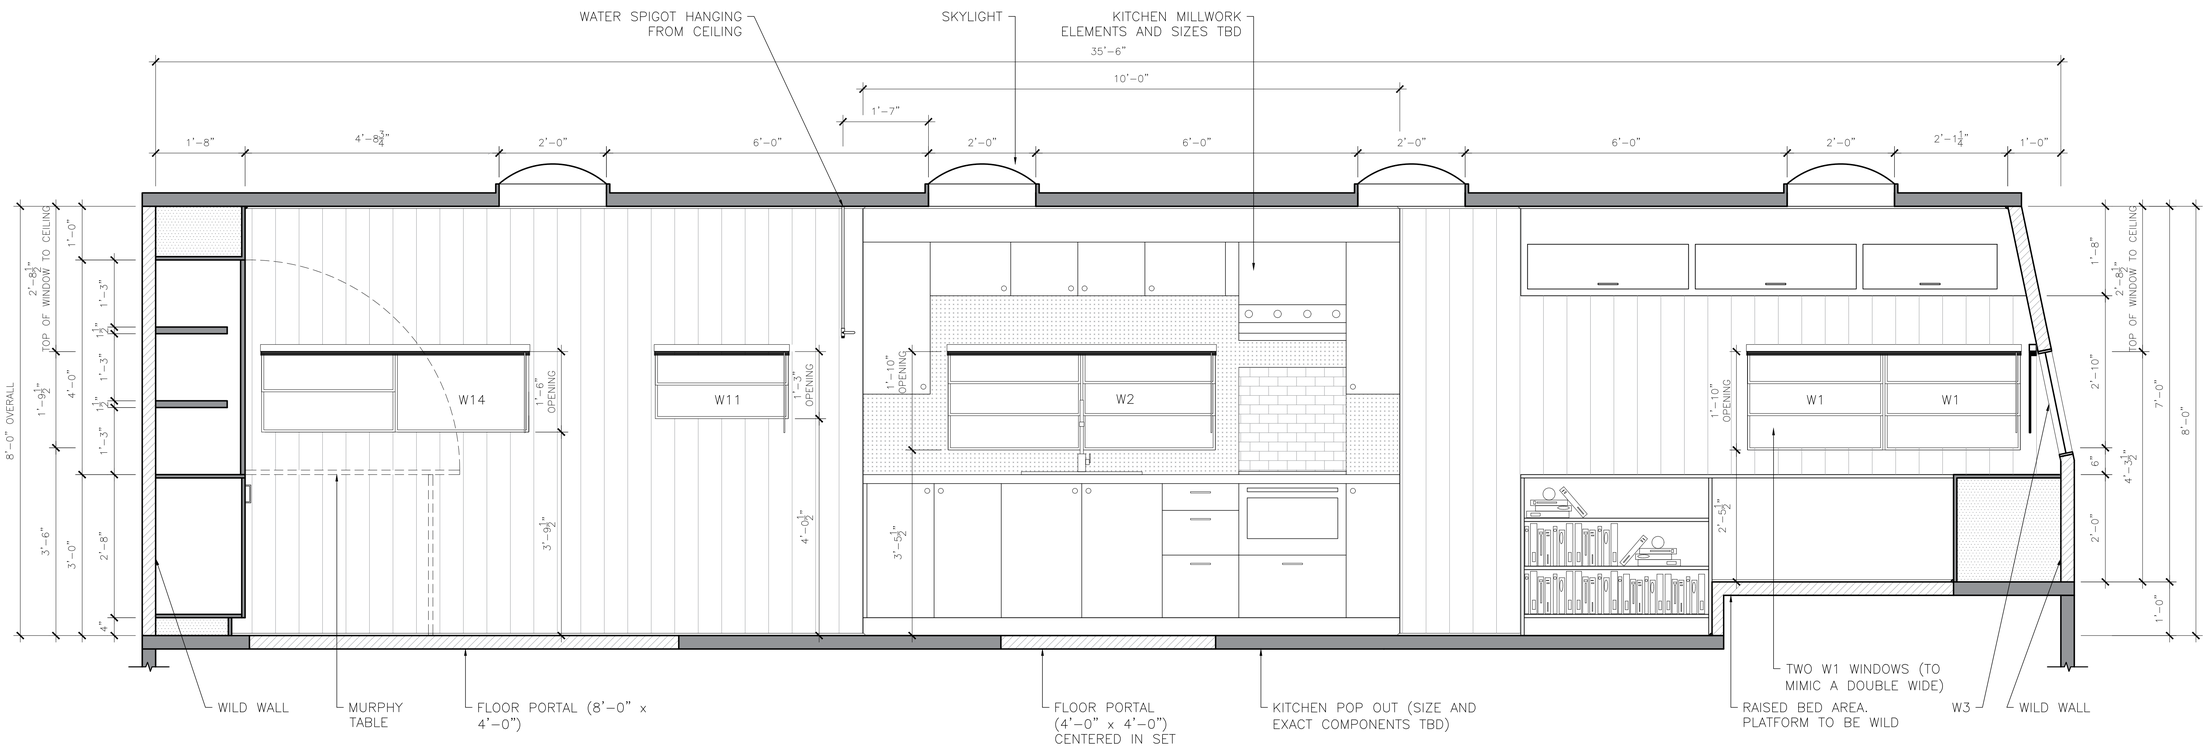

1 / 201 BACK WALL SECTION
SCALE: 3/4" = 1'-0"

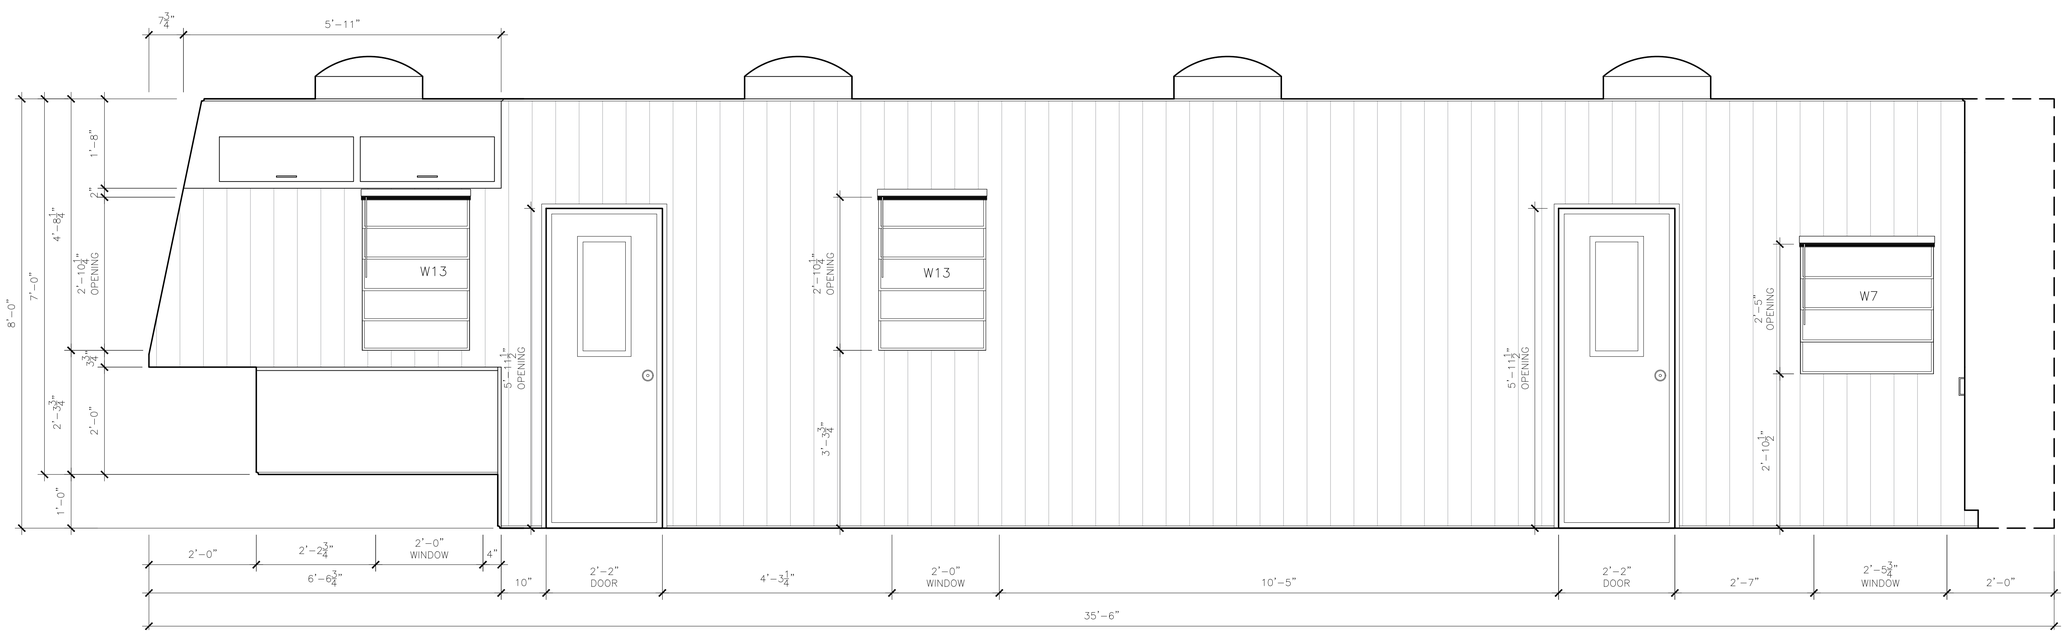

2 / 201 FRONT WALL ELEVATION
SCALE: 3/4" = 1'-0"

GENERAL NOTES
1. CEILING TO BE CONSTRUCTED WITH 2"x4" STUDS TO BEAR WEIGHT OF DRESSING, ACTORS, CREW, ETC.

ISSUED
AUG 08/22

ORPHAN BLACK: ECHOES	ORPHAN BLACK SPINOFF PRODUCTIONS LTD. 2480 STANFIELD RD. MISSISSAUGA, ON. L5Y1S2 T: 647.689.8010	Production Designer: AIDAN LEROUX	Set name.: INT. LUCY'S TRAILER	Date: AUG 08, 2022	Scale: AS NOTED	Revised:	Revision no.:	Set no.: S005	Sheet no.: 201
		Art Director: ALDER DUNLAP	Location address: STUDIO	Drawn by: E.S.	Sheet name: ELEVATIONS				