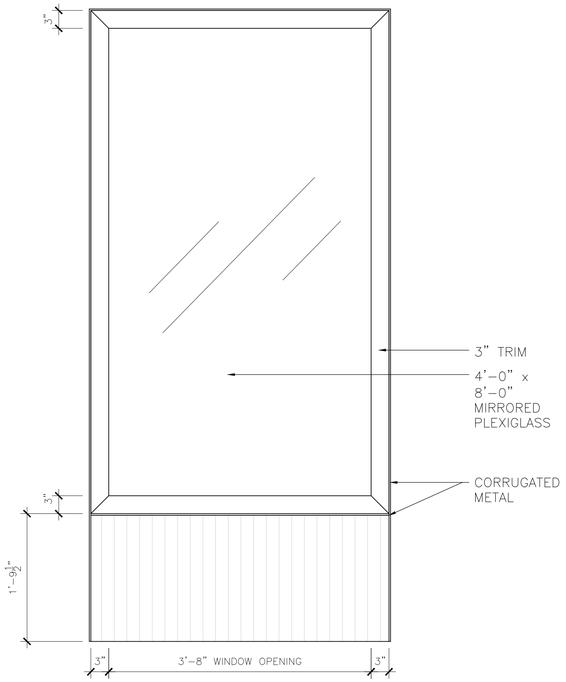

1 / 201 SKYLIGHT FRONT ELEVATION
SCALE: 1" = 1'–0"

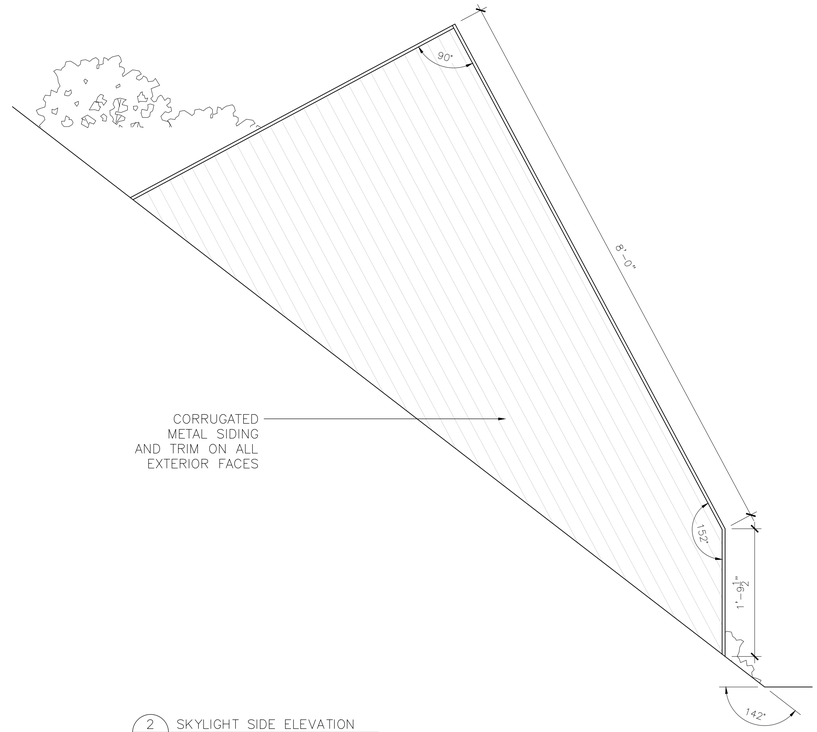

2 / 201 SKYLIGHT SIDE ELEVATION
SCALE: 1" = 1'–0"

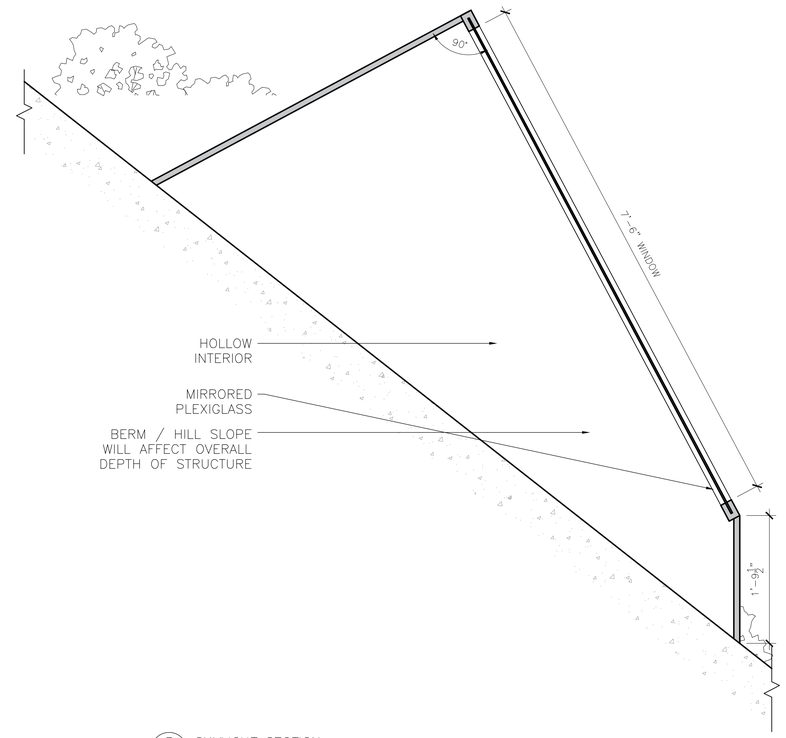

3 / 201 SKYLIGHT SECTION
SCALE: 1" = 1'–0"

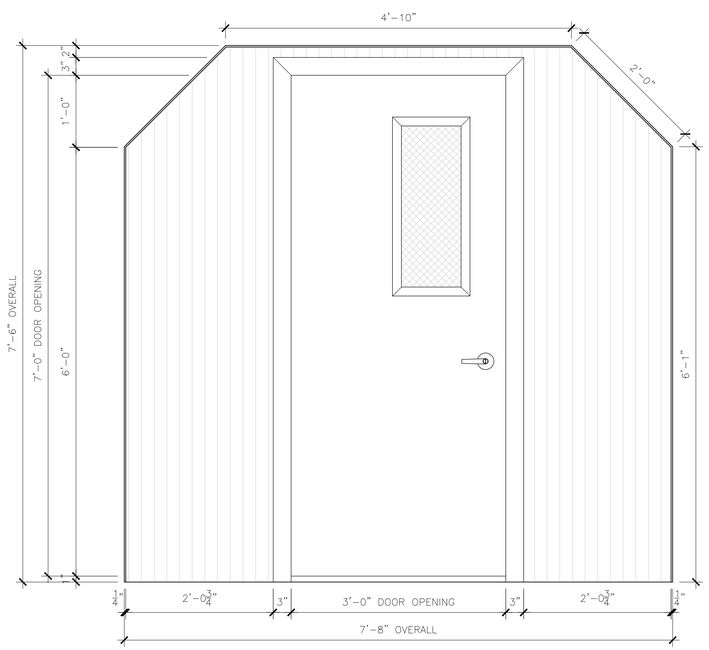

4 / 201 DOORWAY FRONT ELEVATION
SCALE: 1" = 1'–0"

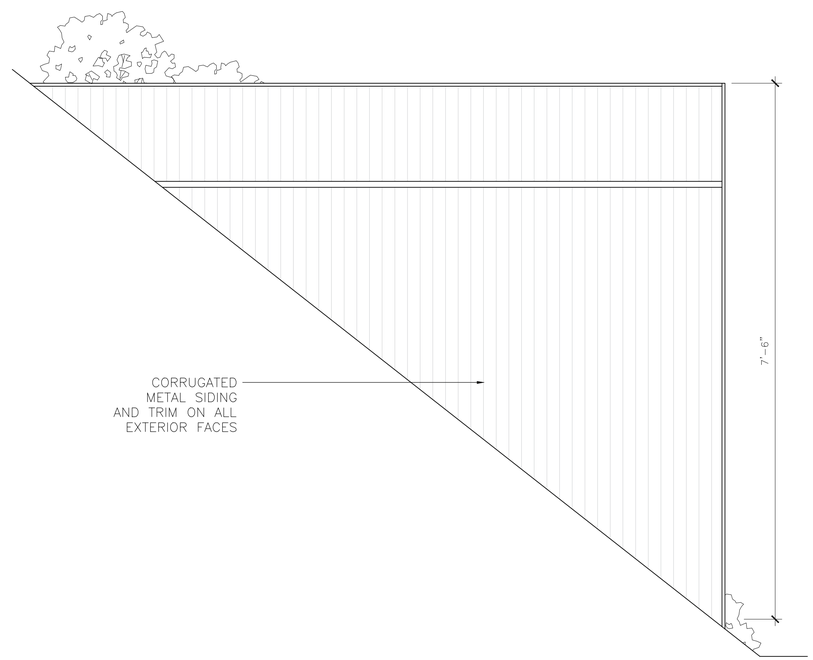

5 / 201 DOORWAY SIDE ELEVATION
SCALE: 1" = 1'–0"

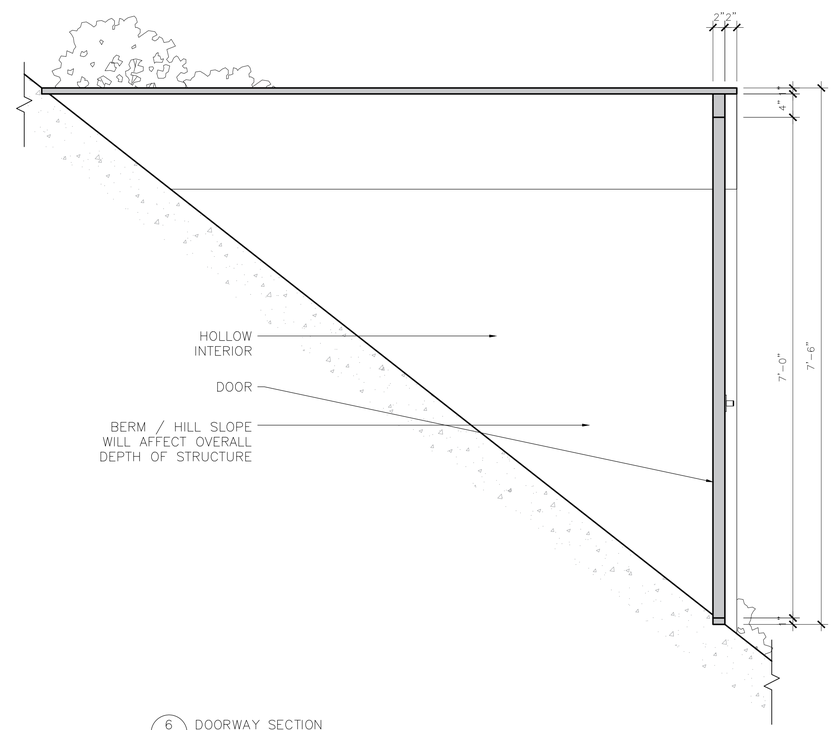

6 / 201 DOORWAY SECTION
SCALE: 1" = 1'–0"

ISSUED
AUG 18/22

GENERAL NOTES
1. MATERIAL TO BE CUT ON LOCATION TO FIT SLOPE OF HILL
2. CONSTRUCTION TO MAKE: 1 x DOORWAY & 3 x SKYLIGHTS

ORPHAN BLACK: ECHOES	ORPHAN BLACK SPINOFF PRODUCTIONS LTD. 2480 STANFIELD RD. MISSISSAUGA, ON, L9Y1S2 T: 647.689.5010	Production Designer: AIDAN LEROUX	Set name.: EXT. BARROS COMPOUND - HILLSIDE	Date: AUG 18, 2022	Scale: AS NOTED	Revised:	Revision no.:	Set no.: 0222	Sheet no.: 201
		Art Director: ALDER DUNLAP	Location address: 16680 KENNEDY RD. N, CALEDON, ON	Drawn by: E.S.	Sheet name: ELEVATIONS & SECTIONS				