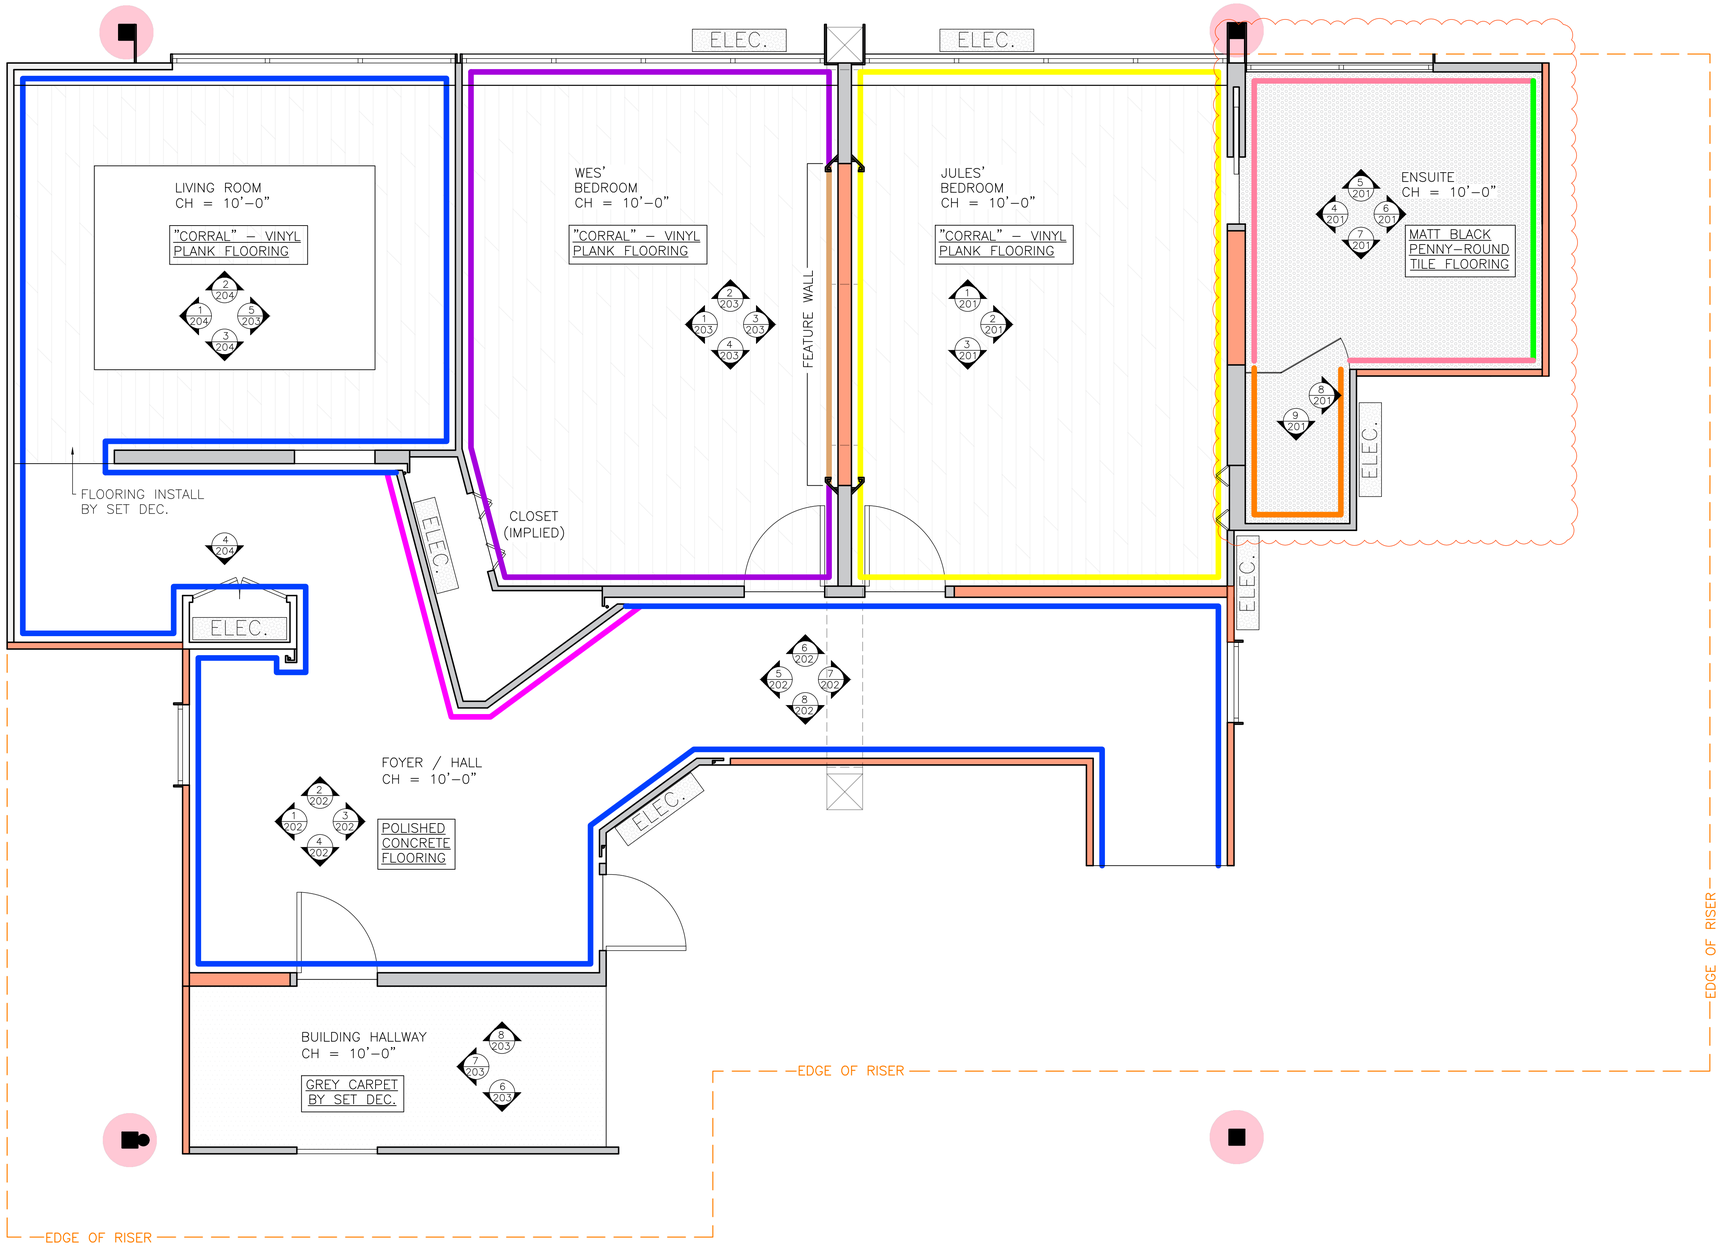

1/402 FINISHES PLAN
SCALE: 3/8" = 1'–0"

FINISH LEGEND

HEATHERED WOOL - OG0613
WALLPAPER BY ANTONINA VELLA
1795 SQ.FT (FOYER / HALLWAY)

WEATHERED - OG0508
WALLPAPER BY ANTONINA VELLA
170 SQ.FT (FOYER FEATURE)

TBD

WALL FINISH C (PAINT TBD)
*** SQ.FT (ENSUITE)

HORIZON - VA1275
WALLPAPER BY AVIVA STANOFF
111 SQ.FT (ENSUITE)

ABACA WEAVE - OG0620
WALLPAPER BY ANTONIA VELLA
540 SQ.FT (WES' BEDROOM)

MODERN ART - NA0563
WALLPAPER BY CANDICE OLSEN
600 SQ.FT (JULES' BEDROOM)

INNER BEAUTY - NA0593
WALLPAPER BY CANDICE OLSEN
120 SQ.FT (WES' FEATURE WALL)

12" x 38" LIVING ALLURE LIGHT GREY - SHOWER WALL TILE BY S&S
120 SQ.FT (SHOWER WALLS)
GROUT: "#14 BISCUIT" (SANDED) BY MAPEI

MATTE BLACK PENNY-ROUND FLOOR TILE BY S&S
(ENSUITE FLOOR & BENCH)
GROUT: "#9 GREY" (UNSANDED) BY MAPEI

GENERAL NOTES
1. ALL FLOORING TO BE POLISHED CONCRETE UNLESS OTHERWISE NOTED
2. CEILING FINISH TO BE CONCRETE IN FOYER / HALLWAY, AND PLASTER IN REMAINDER OF SET
3. ALL DOORS AND TRIM TO BE PAINTED IN ANODIZED ALUMINUM, MEDIUM BRONZE FINISH UNLESS OTHERWISE NOTED

WALL LEGEND
FIXED WALL
WILD WALL

REVISED
SEP 29/22

ORPHAN BLACK: ECHOES

ORPHAN BLACK SPINOFF PRODUCTIONS LTD.
2480 STANFIELD RD.
MISSISSAUGA, ON, L9Y1S2
T: 647.689.8010

Production Designer:	Set name.:	Date:	Scale:	Revised:	Revision no.:	Set no.:	Sheet no.:
AIDAN LEROUX	INT: JULES' CONDO	SEP 14, 2022	AS NOTED	SEP 29, 2022	04	S041	402
Art Director:	Location address:	Drawn by:	Sheet name:				
ALDER DUNLAP	STUDIO	E.S.	FINISHES PLAN				