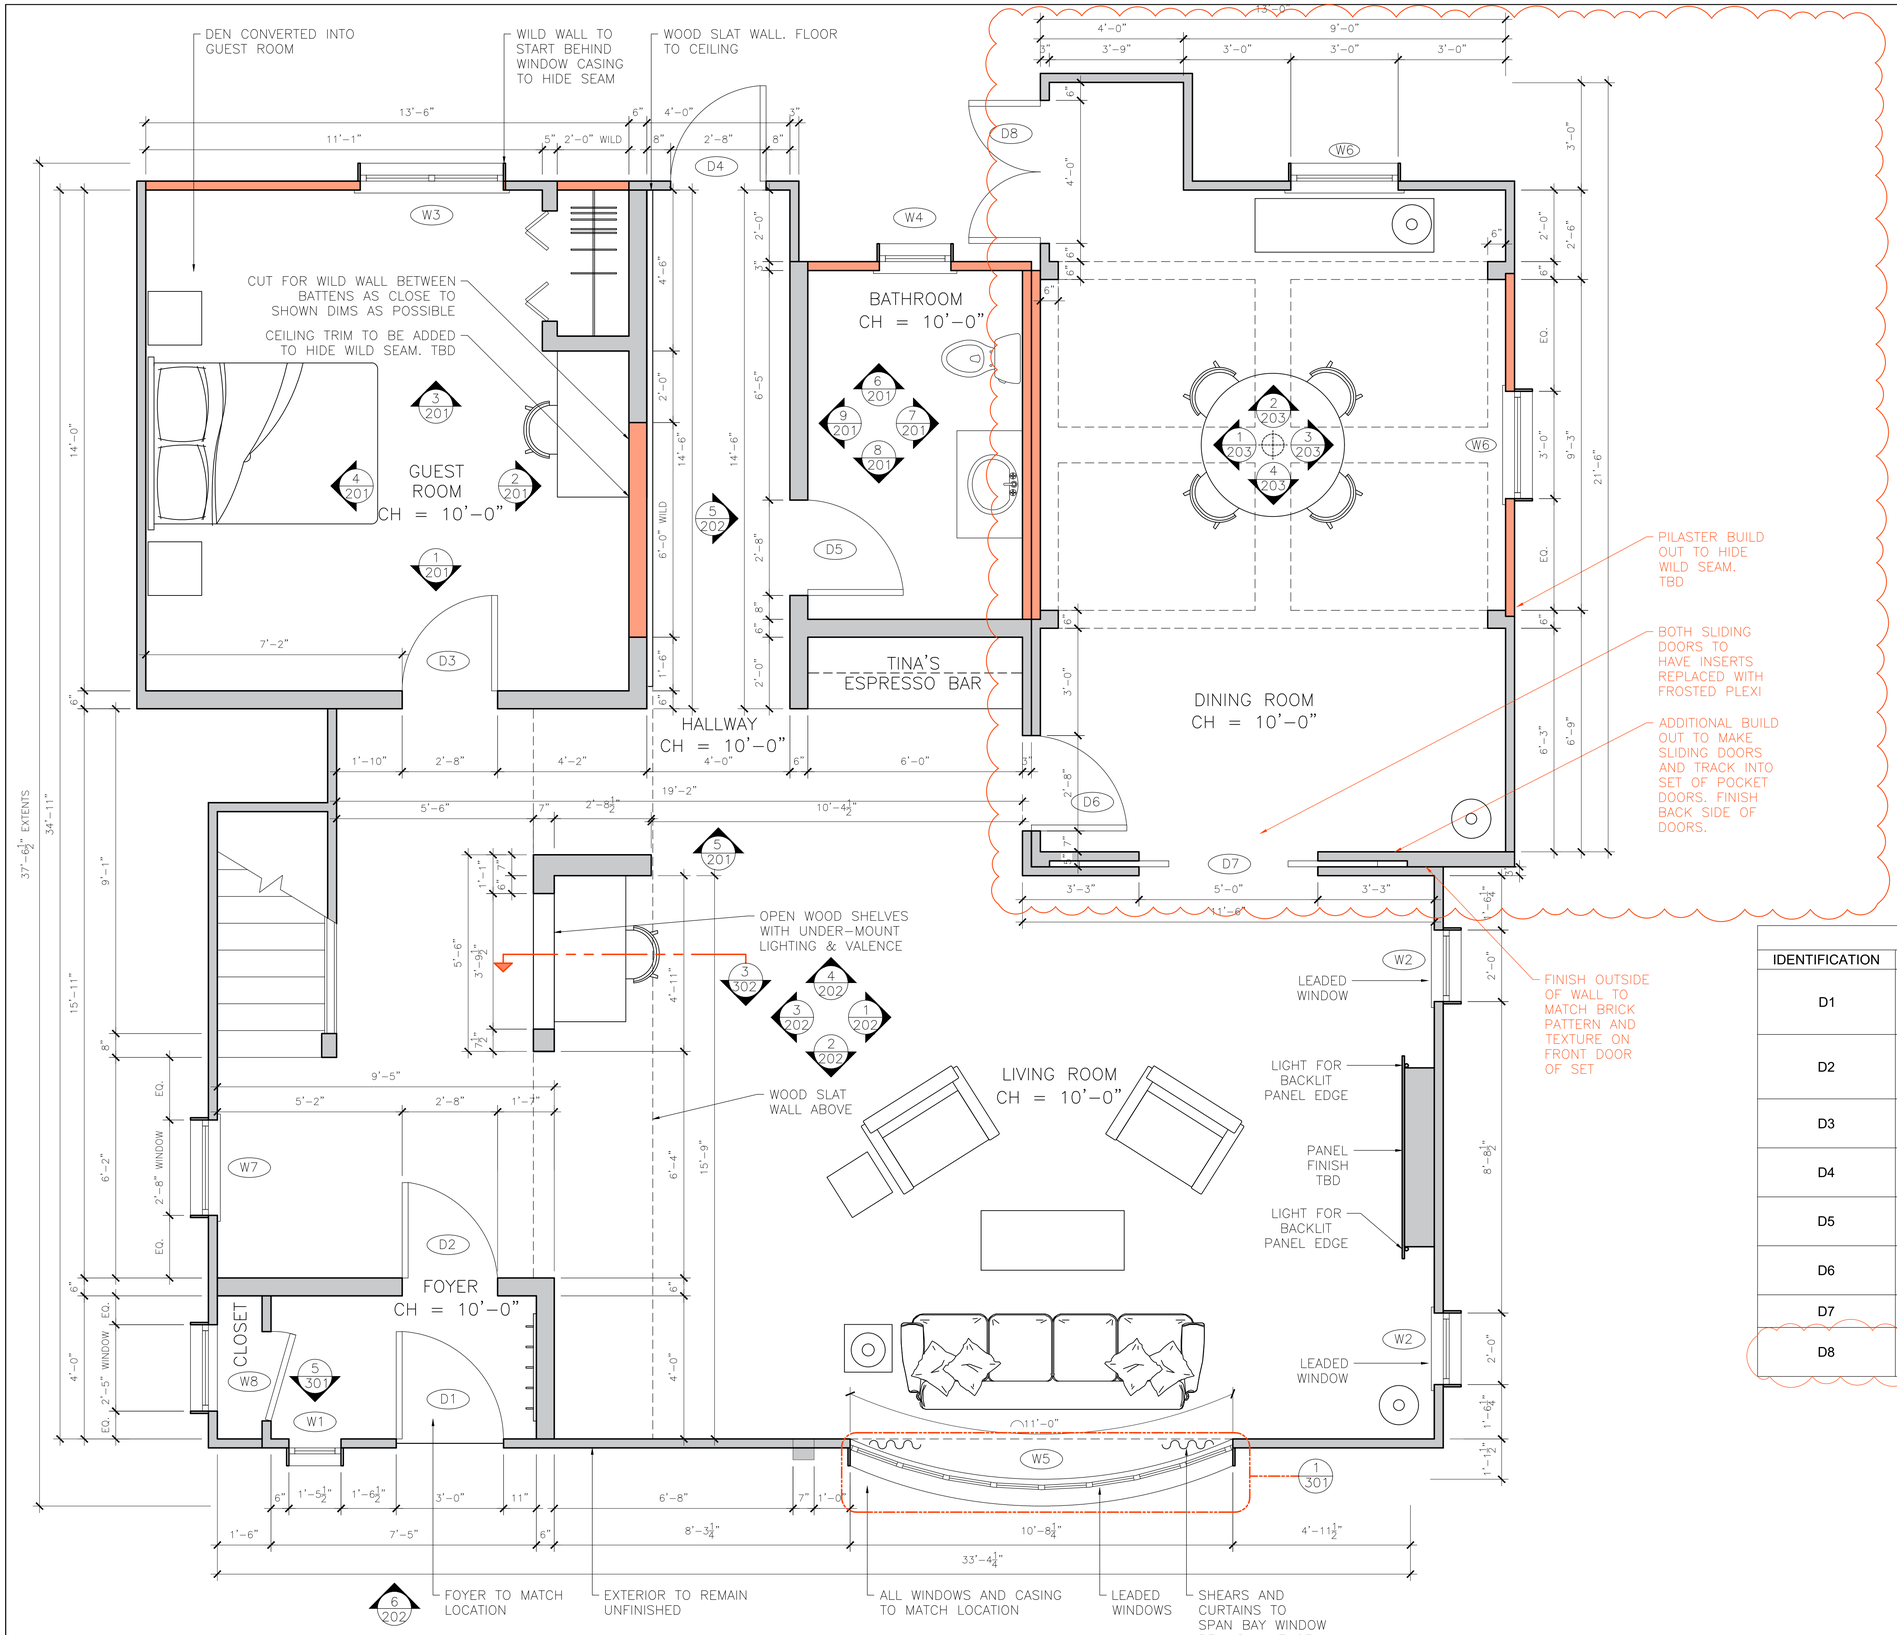

1 / 101 INT. TINA'S HOUSE FLOOR PLAN
SCALE: 1/2" = 1'-0"

TINA'S HOUSE – CONSTRUCTION NOTES

- ADDITIONAL DINING AND KITCHEN AREA TO BE BUILT ONTO EXISTING S020 SET IN STUDIO WHERE INDICATED
- PARTITION WHERE SLIDING DOORS ARE CURRENTLY INSTALLED IS TO BE BE BUILT UP TO RESEMBLE POCKET DOOR WALL. SLIDING DOORS AND HARDWARE TO PLAY AS POCKET DOORS
- BASE, CASING, AND JAMBS TO MATCH REMAINDER OF EXISTING SET
- WINDOWS (W6, W7, & W8) TO BE INSTALLED, SEE WINDOW SCHEDULE BELOW FOR DETAILS
- RETROFIT EXISTING WALLS TO WILD WHERE INDICATED ON REVISED PLAN

TINA'S HOUSE – SCENIC NOTES

- EXISTING DOORS LEADING INTO NEW DINGING AND KITCHEN AREA TO BE PAINTED ON BOTH SIDES TO MATCH
- ALL TRIM TO MATCH REMAINDER OF SET: **PARA P2139-03 "WEATHERVANE"**
- NEW WINDOW (W7) TO HAVE FROSTING APPLIED
- DINING ROOM WALLPAPER TO MATCH LIVING ROOM, "DEEP BLUE – NATURAL GRASSCLOTH" BY MONARQUE

TINA'S HOUSE – SET DEC. NOTES

- KITCHEN CABINETS AND ACCESSORIES TO BE PROVIDED BY SET DEC.
- VINYL FLOORING TO EXTEND INTO NEW DINING AND KITCHEN AREA FROM LIVING ROOM

WINDOW SCHEDULE

IDENTIFICATION	HEIGHT	WIDTH	STATE	FINISH	NOTES
W1	1'-6"	1'-5 1/2"	NEW	CLEAR	LEADED, TO MATCH LOCATION
W2	4'-0"	2'-0"	NEW	FROSTED	QTY x 2, LEADED, STYLED LIKE LOCATION WINDOWS
W3	4'-0"	4'-0"	NEW	CLEAR	
W4	3'-0"	2'-0"	NEW	FROSTED	
W5	SEE 301	SEE 301	NEW	CLEAR	LEADED, TO MATCH LOCATION. SEE DETAIL DRAWINGS
W6	4'-0"	3'-0"	NEW	CLEAR	QTY x 2
W7	4'-0"	2'-8"	EXISTING	FROSTED	APPLY FROSTING, 3'-0" A.F.F
W8	4'-0"	2'-5"	EXISTING	CLEAR	3'-0" A.F.F

DOOR SCHEDULE

IDENTIFICATION	HEIGHT	WIDTH	STATE	FINISH	SWING	NOTES
D1	SEE 302	SEE 302	NEW	PAINTED TO MATCH LOCATION	LEFT	ENTRY HARDWARE (HD), LOCK, LEADED GLASS INSERT, TO MATCH LOCATION
D2	6'-8"	2'-8"	NEW	PARA P2139-03 "WEATHERVANE"	LEFT	PASSAGE HD, 4 LITE PRIVACY GLASS, HOME DEPOT #1000812334
D3	6'-8"	2'-8"	NEW	PARA P2139-03 "WEATHERVANE"	RIGHT	PASSAGE HD, 4 LITE PRIVACY GLASS, HOME DEPOT #1000812334
D4	6'-8"	2'-8"	NEW	PARA P2139-03 "WEATHERVANE"	RIGHT	ENTRY HD, LOCK, HOME DEPOT #1001057733
D5	6'-8"	2'-8"	NEW	PARA P2139-03 "WEATHERVANE"	RIGHT	PRIVACY HD, 4 PANEL, HOME DEPOT #1000755960
D6	6'-8"	2'-8"	NEW	PARA P2139-03 "WEATHERVANE"	RIGHT	PASSAGE HD, 4 PANEL, HOME DEPOT #1000755960
D7	6'-8 1/2"	5'-0"	NEW	PARA P2139-03 "WEATHERVANE"	SLIDE	HD TBD, HOME DEPOT #1001319410
D8	6'-8"	2'-8"	NEW	PARA P2139-03 "WEATHERVANE"	RIGHT	PASSAGE HD, HOME DEPOT #1000755960

WALL LEGEND

- FIXED WALL
- WILD WALL

GENERAL NOTES

1. SET FOYER, LIVING ROOM AND OTHER INTERIOR ELEMENTS MAY REQUIRE MINOR REVISIONS TO MATCH LOCATION ONCE CONFIRMED.
2. ALL DOORS TO BE PRACTICAL UNLESS OTHERWISE NOTED.
3. ALL DOOR HARDWARE TBD BY SET DEC. UNLESS OTHERWISE NOTED.
4. ALL FOYER FLOORING, BASE TRIM, AND CASING TO BE MATCHED TO LOCATION ONCE DETERMINED.

REVISED
OCT 05/22

ORPHAN BLACK: ECHOES

ORPHAN BLACK SPINOFF PRODUCTIONS LTD.
2480 STANFIELD RD.
MISSISSAUGA, ON, L5Y1S2
T: 647.689.8010

Production Designer: AIDAN LEROUX	Set name.: INT. TINA'S HOUSE	Date: AUG 22, 2022	Scale: AS NOTED	Revised: OCT 05, 2022	Revision no.: 03	Set no.: S020	Sheet no.: 101
Art Director: ALDER DUNLAP	Location address: STUDIO	Drawn by: E.S.	Sheet name: FLOOR PLAN				