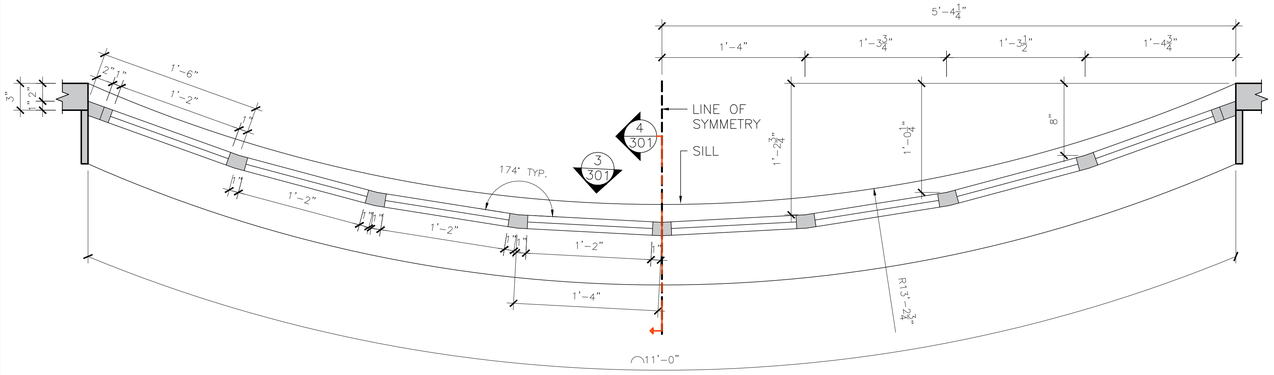

1 / 301 BAY WINDOW PLAN
SCALE: 1-1/2" = 1'-0"

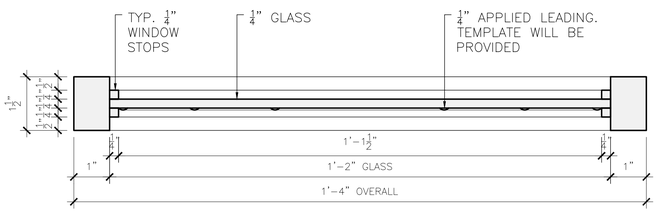

2 / 301 BAY WINDOW PANE SECTION
SCALE: 6" = 1'-0"

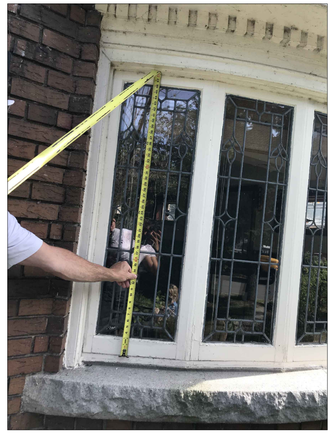

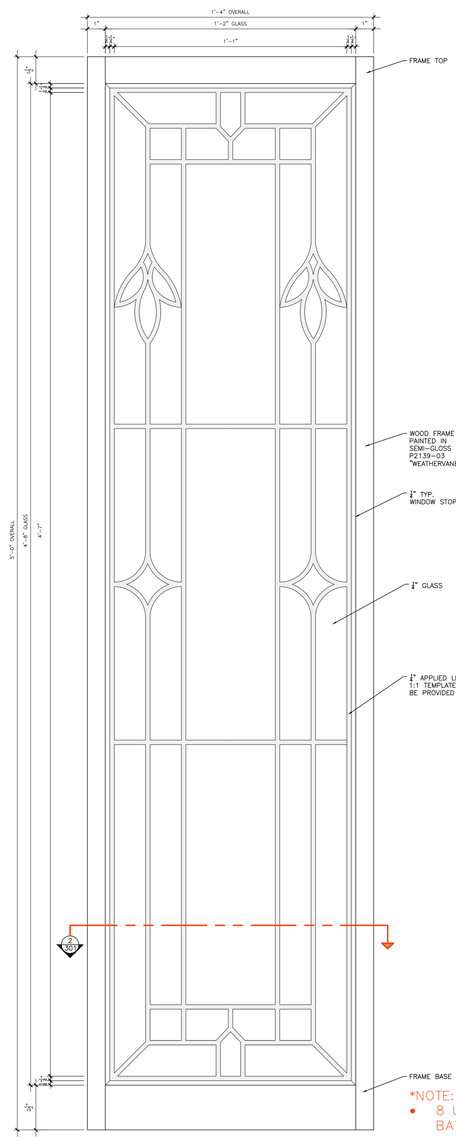

*NOTE:
- 8 UNITS WILL BE REQUIRED FOR BAY WINDOW CONSTRUCTION

3 / 301 BAY WINDOW PANE ELEVATION DETAIL
SCALE: 3" = 1'-0"

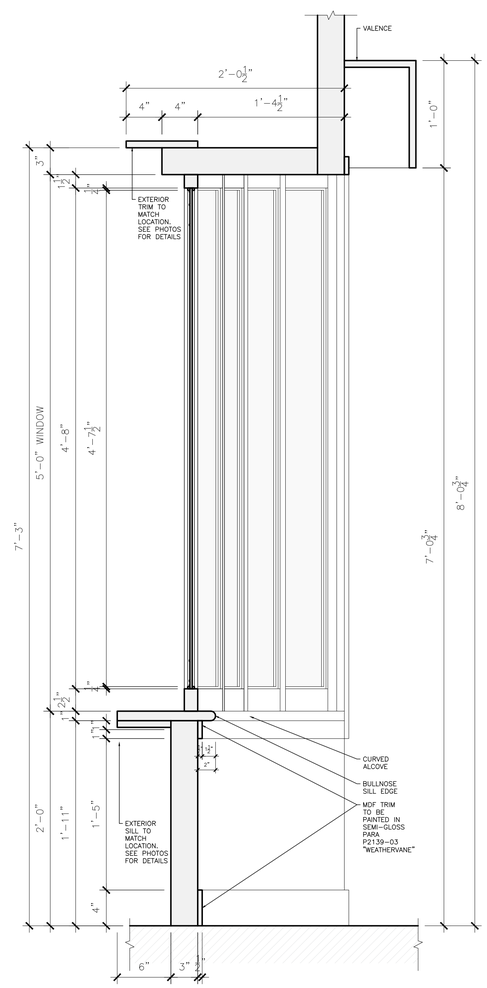

4 / 301 BAY WINDOW TRANSVERSE SECTION
SCALE: 1-1/2" = 1'-0"

GENERAL NOTES
1. BASE TRIM TO BE 4" HIGH PAINTED, FLAT MDF
2. CASING FOR DOORS AND WINDOWS TO BE 2" HIGH PAINTED, FLAT MDF
3. ALL TRIM TO BE PAINTED IN SEMI-GLOSS PARA P2139-03 "WEATHERVANE"
4. WOOD SLATS TO BE STAINED IN A WALNUT FINISH.

REVISED
AUG 23/22

ORPHAN BLACK: ECHOES	ORPHAN BLACK SPINOFF PRODUCTIONS LTD. 2480 STANFIELD RD. MISSISSAUGA, ON, L9Y1S2 T: 647.689.8010	Production Designer: AIDAN LEROUX	Set name.: INT. TINA'S HOUSE	Date: AUG 22, 2022	Scale: AS NOTED	Revised: AUG 23, 2022	Revision no.: 01	Set no.: S020
		Art Director: ALDER DUNLAP	Location address: STUDIO	Drawn by: E.S.	Sheet name: DETAILS			Sheet no.: 301